

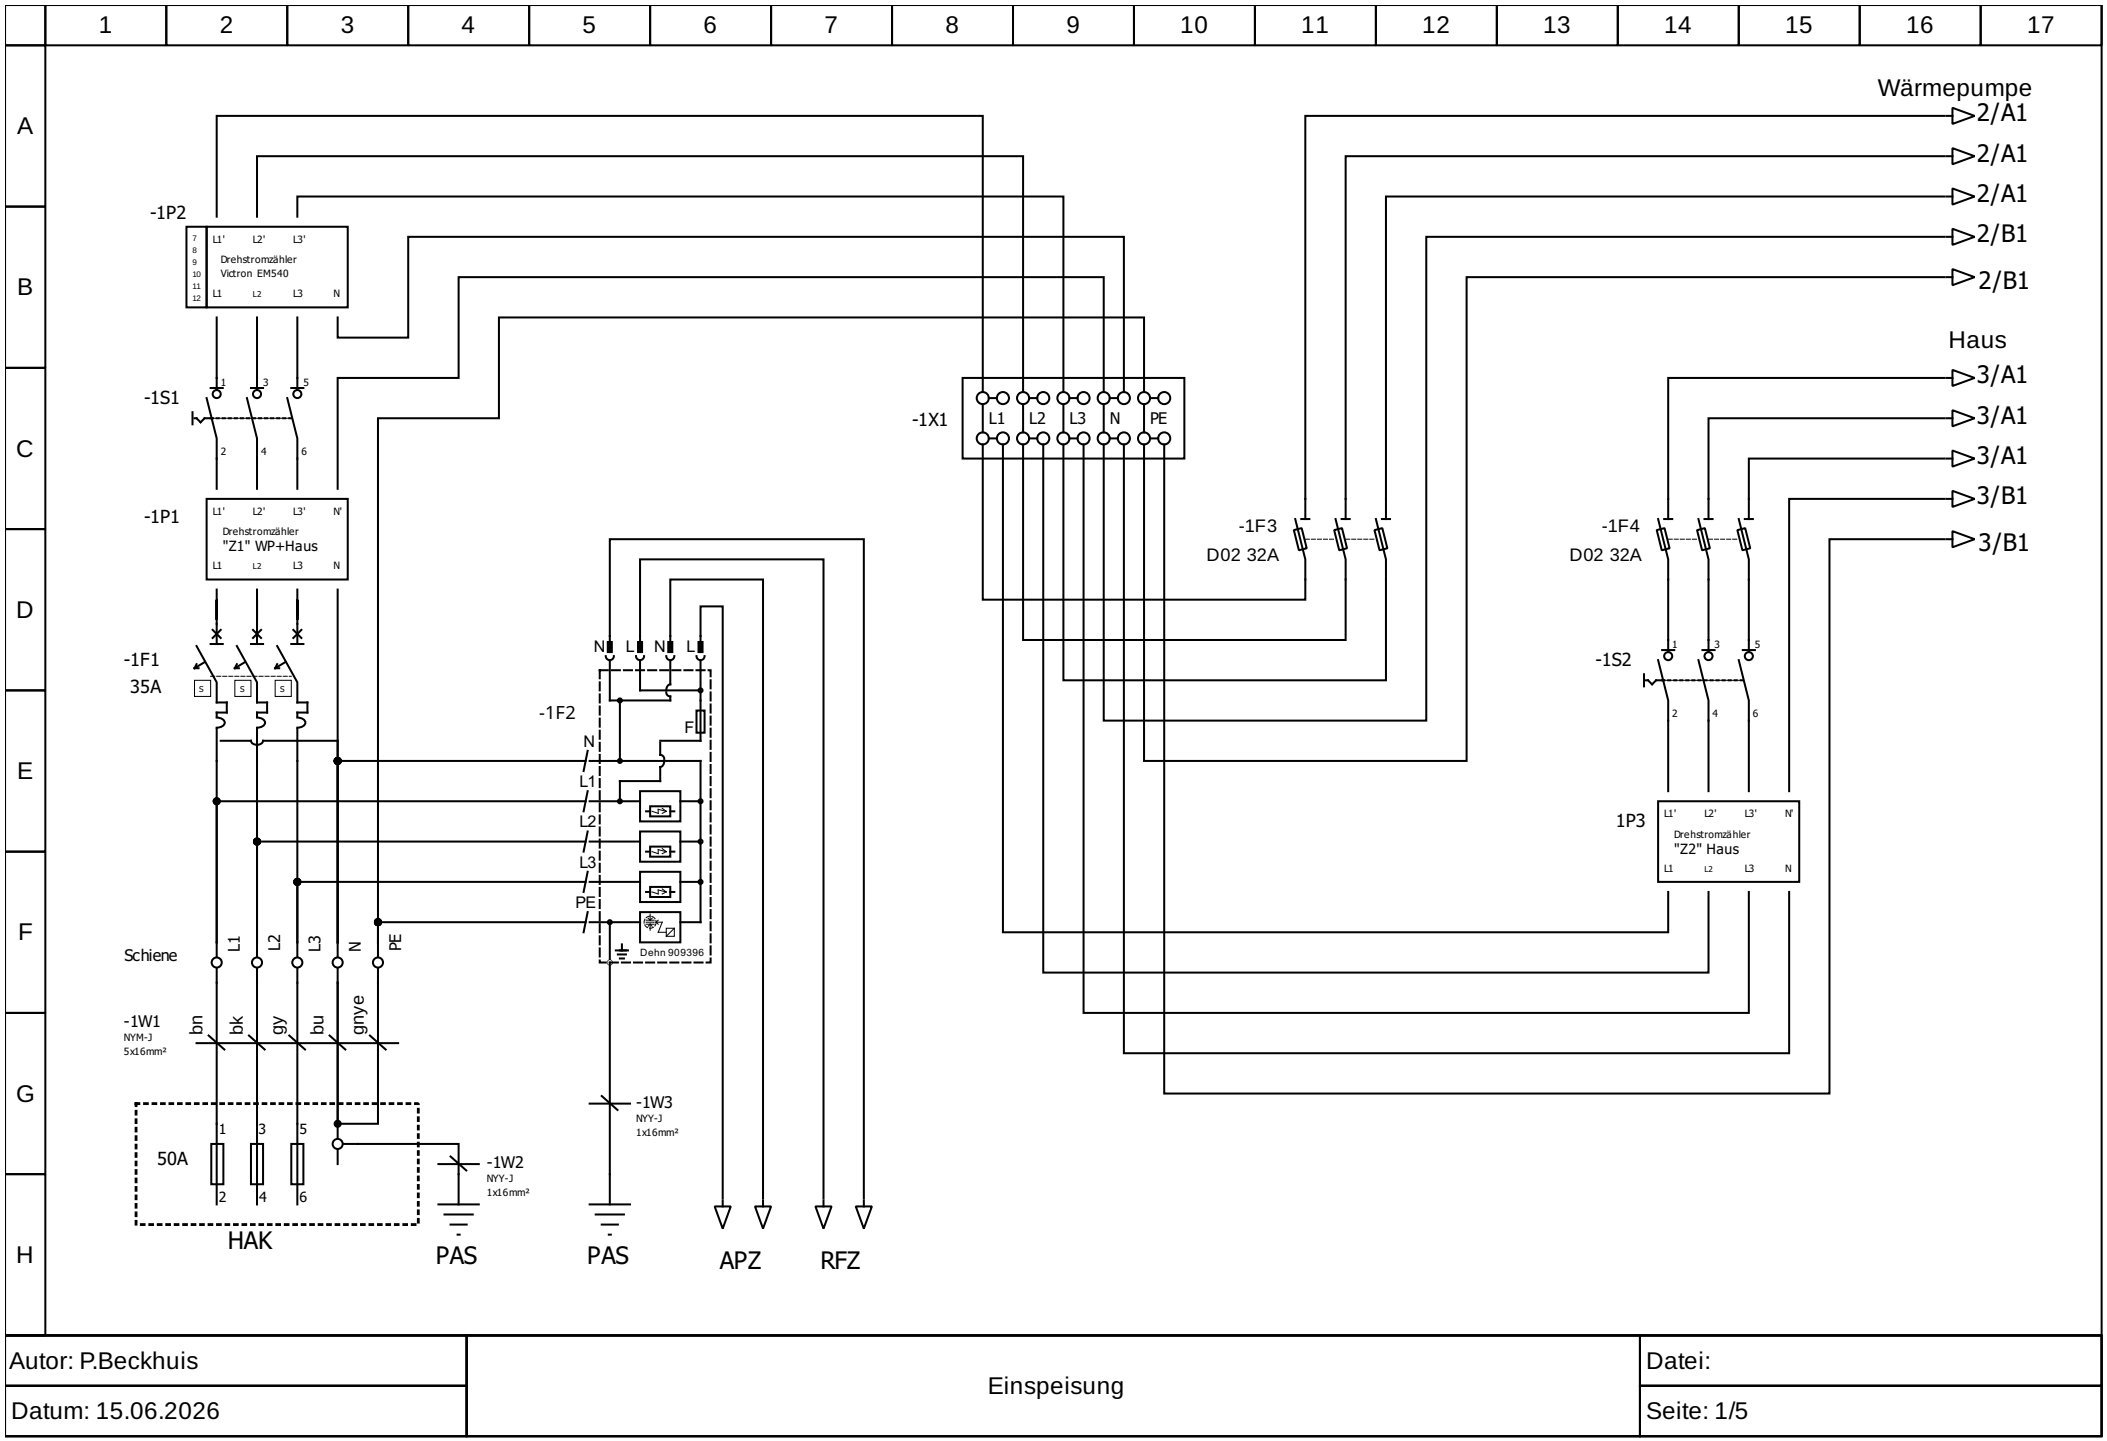



Autor: P.Beckhuis	Einspeisung	Datei:
Datum: 15.06.2026		Seite: 1/5

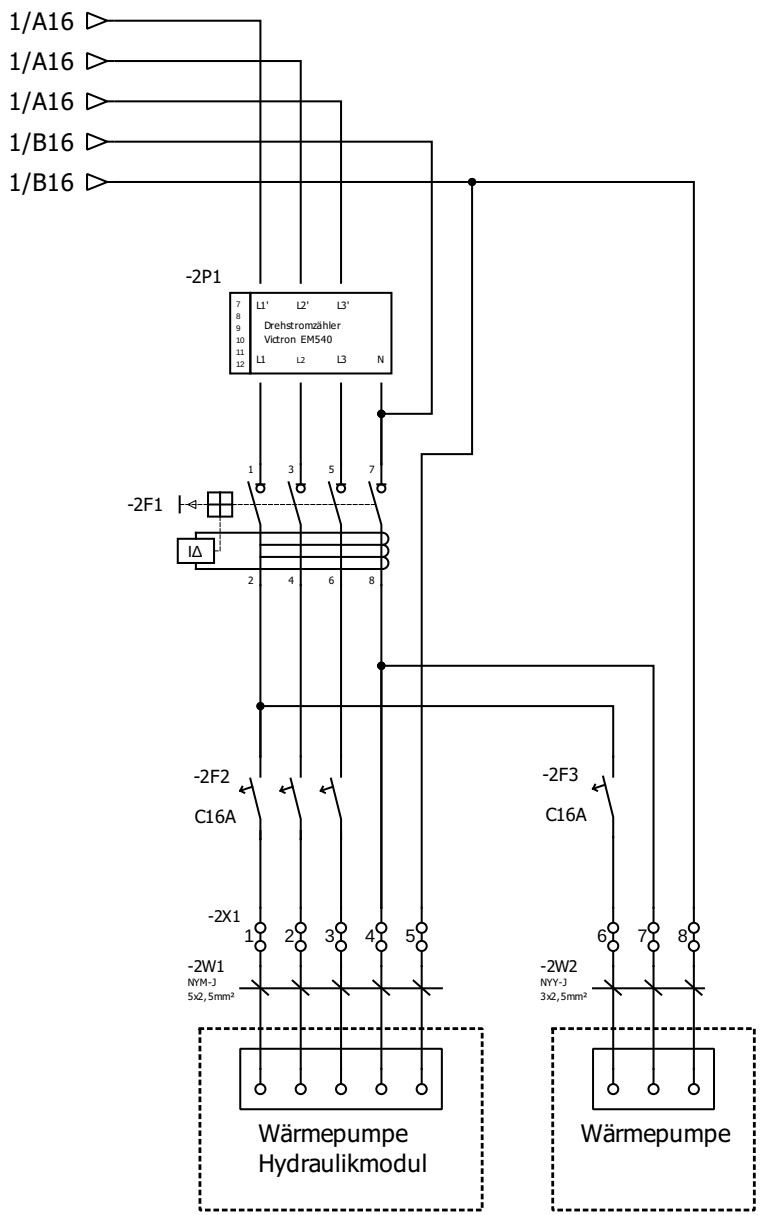

Autor: Beckhuis	Wärmepumpe	Datei:
Datum: 15.06.2026		Seite: 2/5

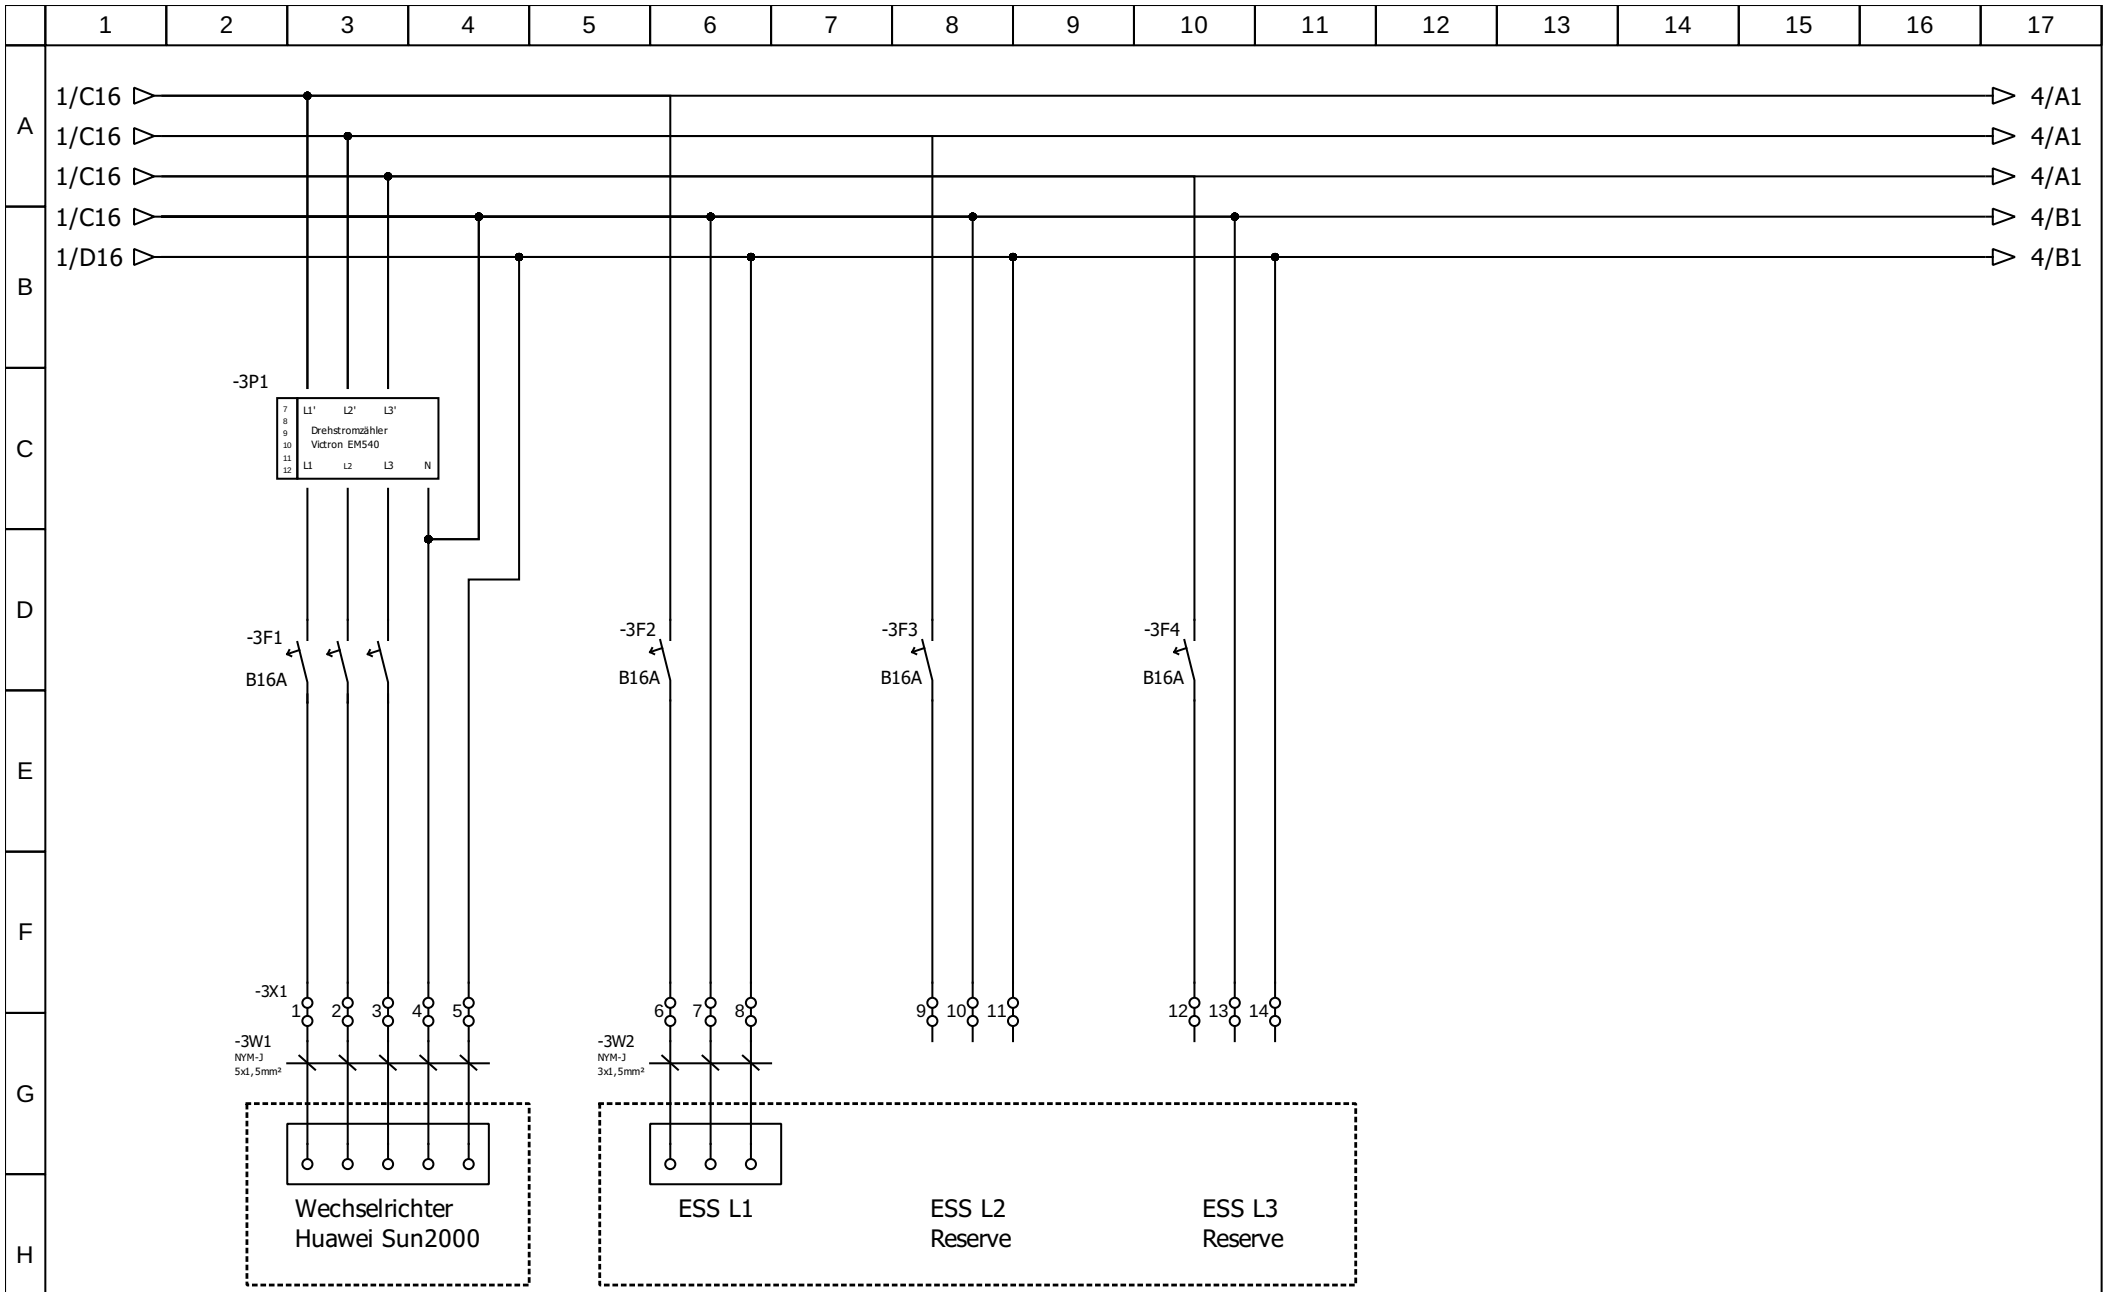

Autor: P.Beckhuis	Photovoltaik	Datei:
Datum: 15.06.2026		Seite: 3/5

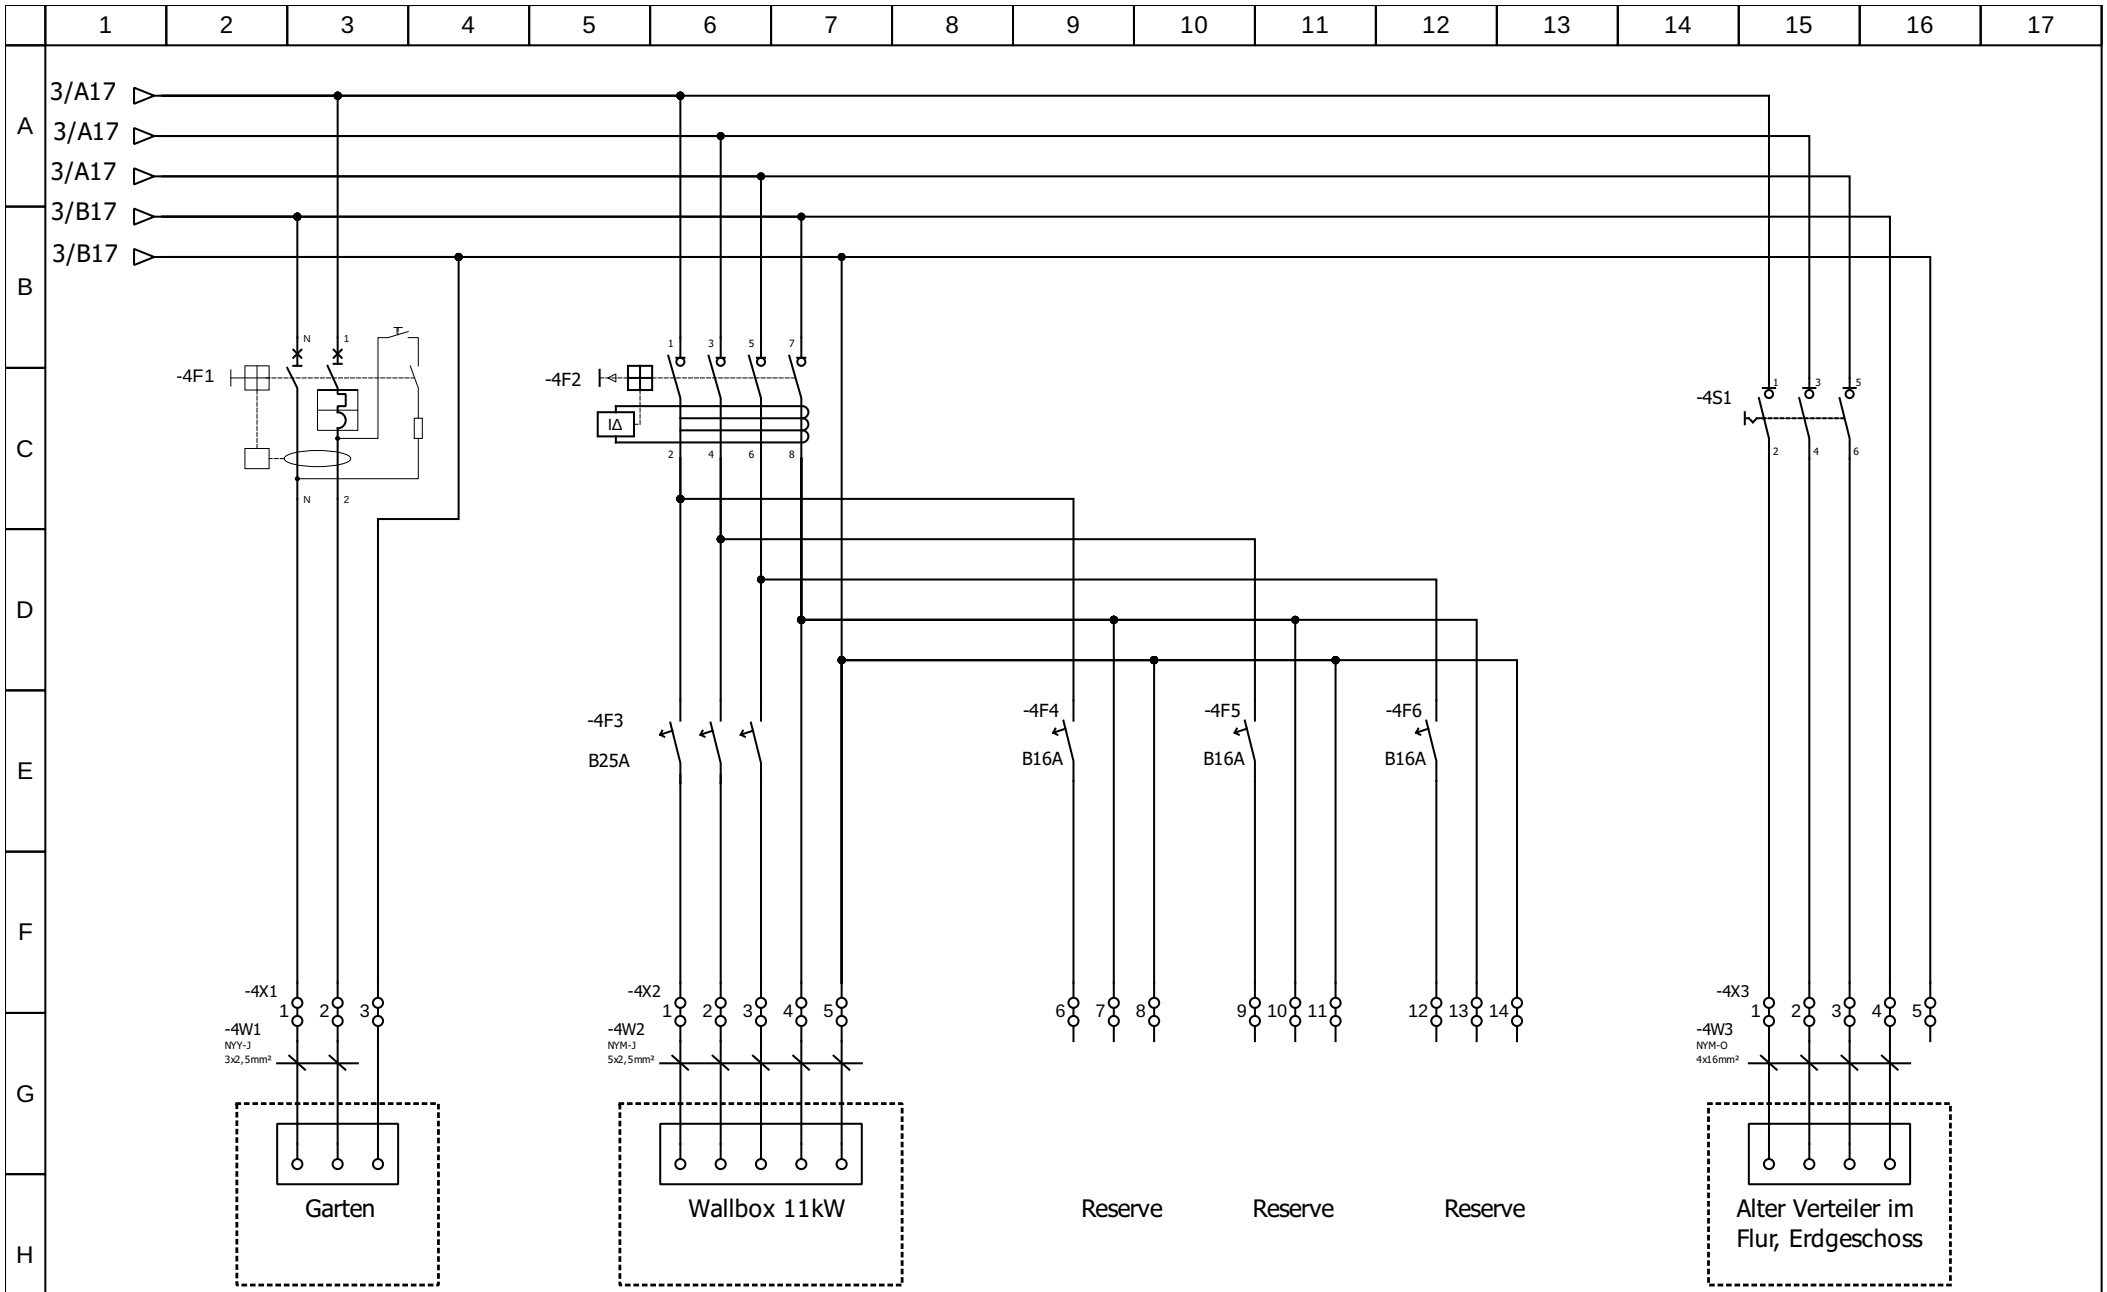

Autor: P.Beckhuis	Haus 1	Datei:
Datum: 15.06.2026		Seite: 4/5

BMK-Legende:

-1F1	SLS Schalter 35A
-1F2	Überspannungsschutz inkl. Vorsicherung APZ/RFZ
-1F3	D02-Sicherungstrenner Wärmepumpe
-1F4	D02-Sicherungstrenner Haus und PV
-1P1	EVU Zähler Z1 (Wärmepumpe + Haus)
-1P2	ESS Smartmeter
-1P3	EVU Zähler Z2 (Haus)
-1S1	Schalter nach Z1
-1S2	Schalter nach Z2
-1X1	Klemmblock nach Z1


-2F1	RCD Typ B Wärmepumpe
-2F2	Vorsicherung Wärmepumpe Hydraulikmodul
-2F3	Vorsicherung Wärmepumpe
-2P1	Wärmepumpe Smartmeter

-3F1	Vorsicherung PV Wechselrichter
-3F2	Vorsicherung ESS
-3F3	Vorsicherung ESS
-3F4	Vorsicherung ESS
-3P1	PV Smartmeter

-4F1	LS-RCD Garten
-4F2	RCD Typ B Haus
-4F3	Vorsicherung Wallbox
-4F4	Vorsicherung Reserve
-4F5	Vorsicherung Reserve
-4F6	Vorsicherung Reserve
-4S1	Schalter Haus alter Verteiler im Flur, EG

Farb-Legende:

Klemmblock
Schalter
Sicherungstrenner
RCD/RCD-LS
Sicherungsautomat
Smartmeter
Sonstige

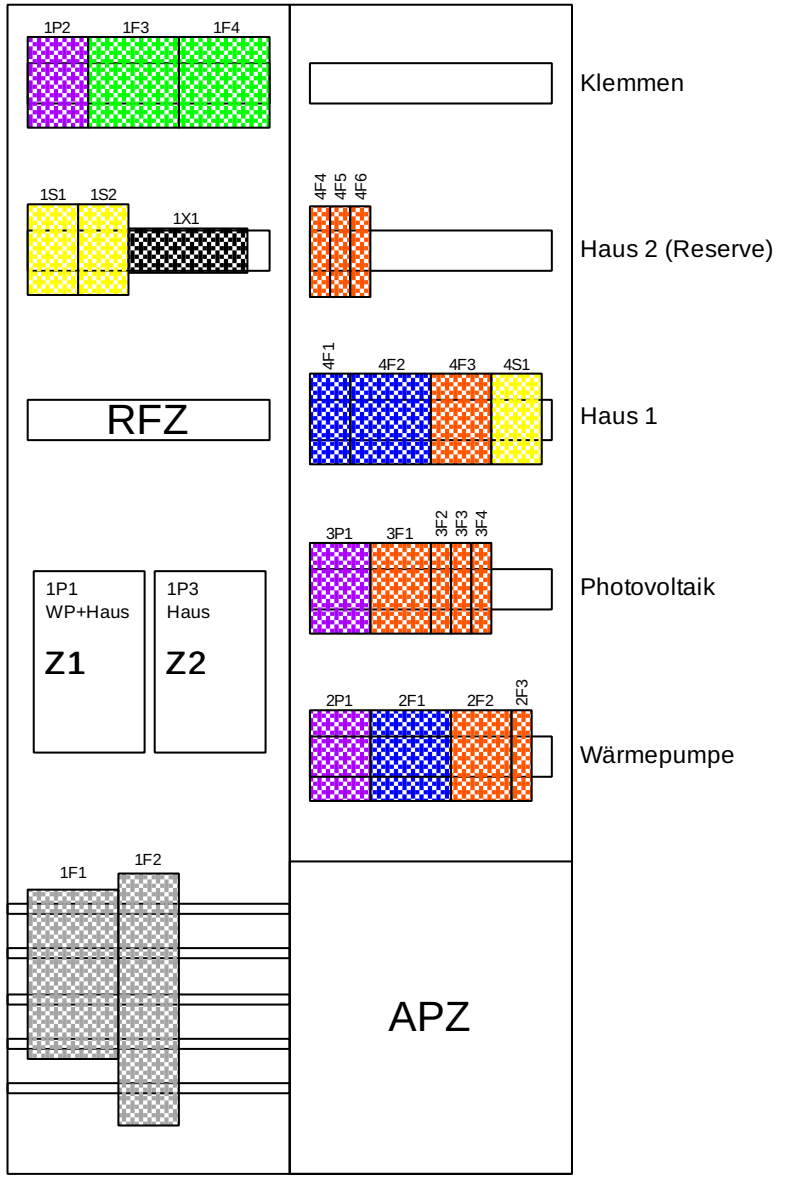

Autor: P.Beckhuis	Schaltschrankansicht	Datei:
Datum: 15.06.2026		Seite: 5/5